


■ 침단부_ MJ81 내부 결선도 (개선 전)_대전역 N68Ap 시범설치



■ **첨단부_ MJ81 내부 결선도 (개선 후)_군북역 N21Ap 시범설치**

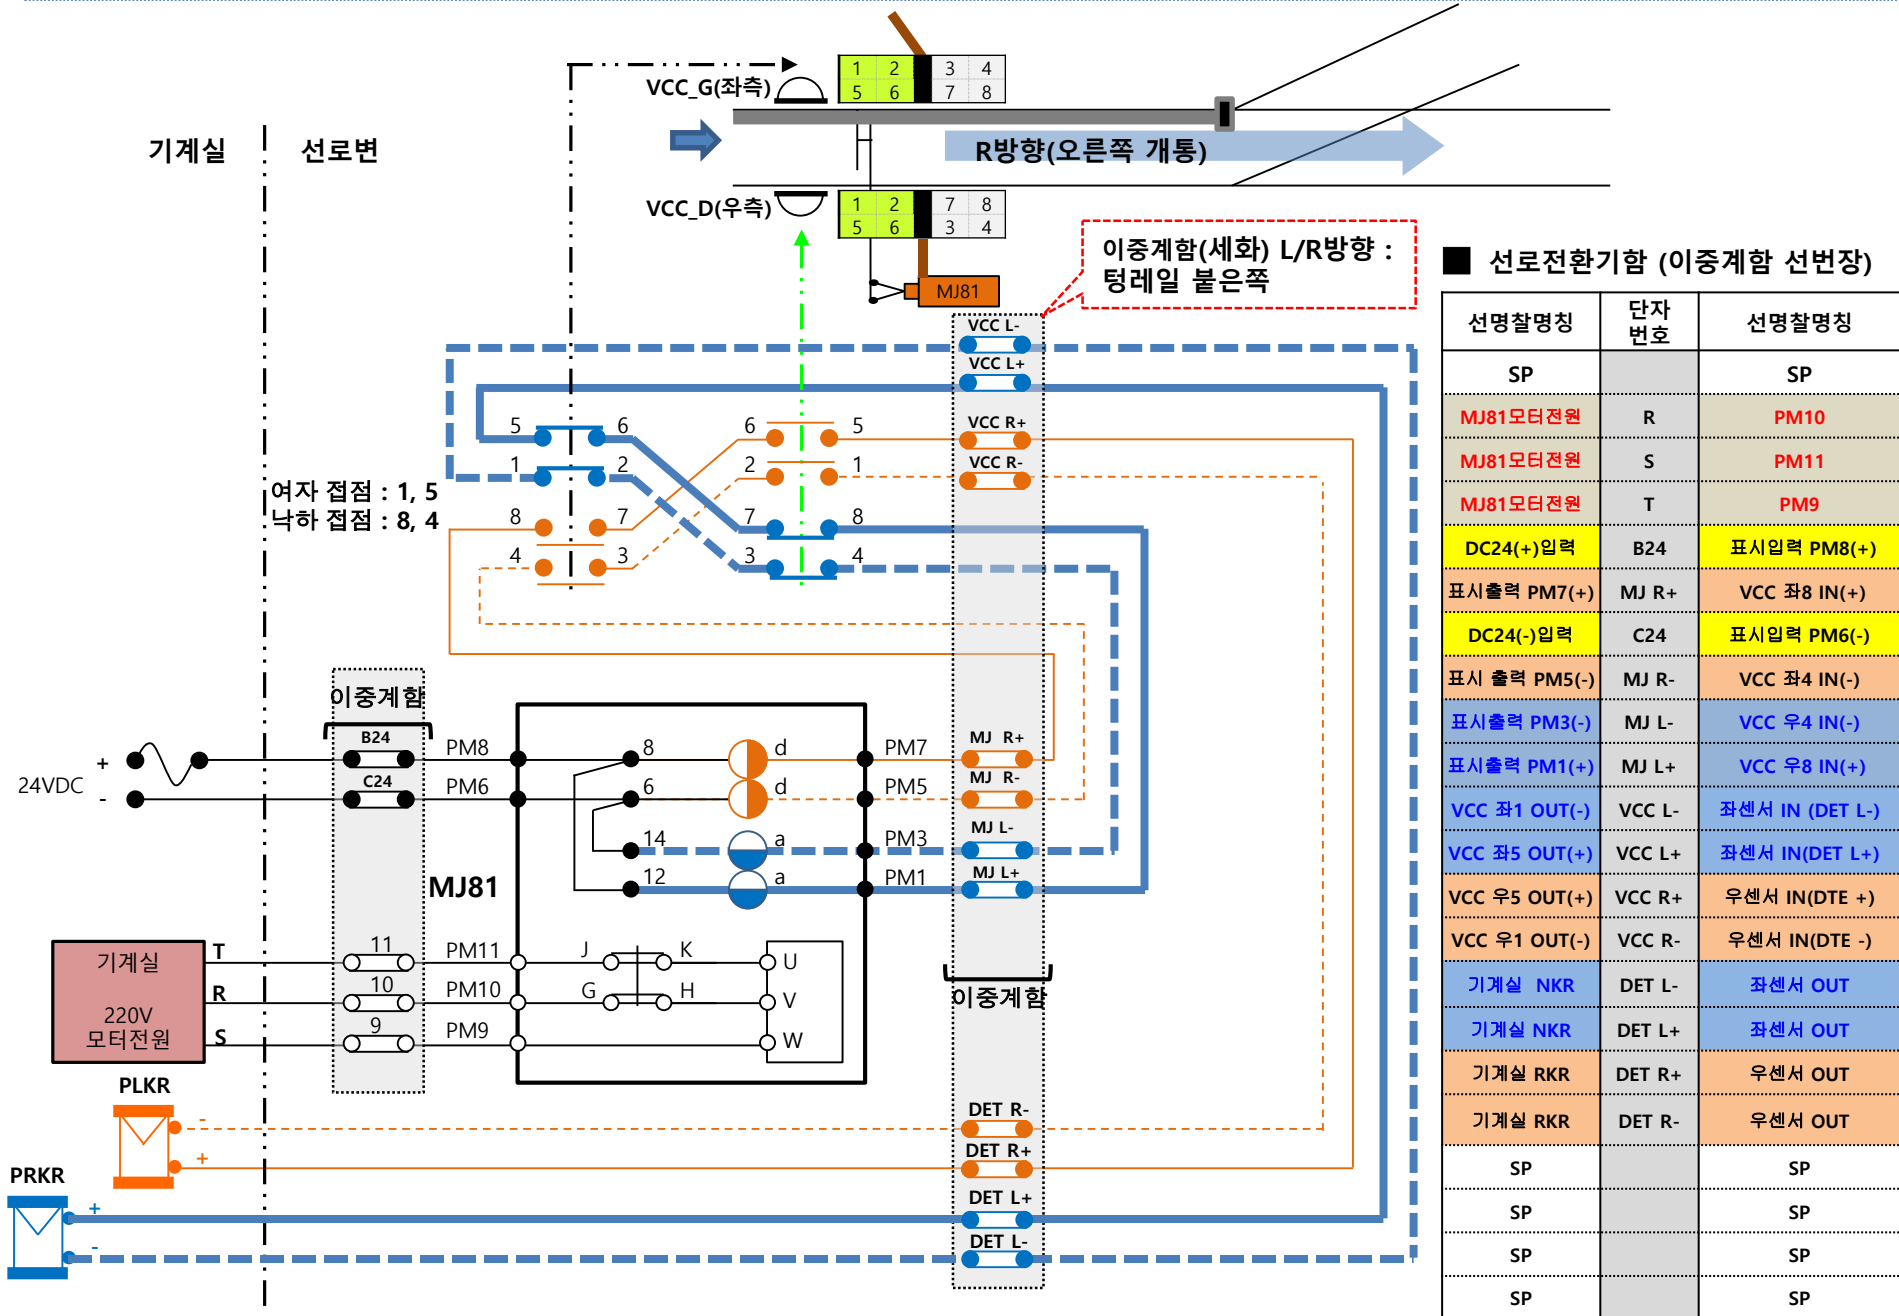